
**CONTROLLED COPY**

| REV.NO. | CHANGE DETAILS | DATE | PREPARED | APPD. |
|---|---|---|---|---|
| 1.0 | INITIAL RELEASE | 12.11.22 | DLR | YS |
| 1.1 | MC18&MC26 WIRING REMOVED | 08.03.23 | DLR | YS |

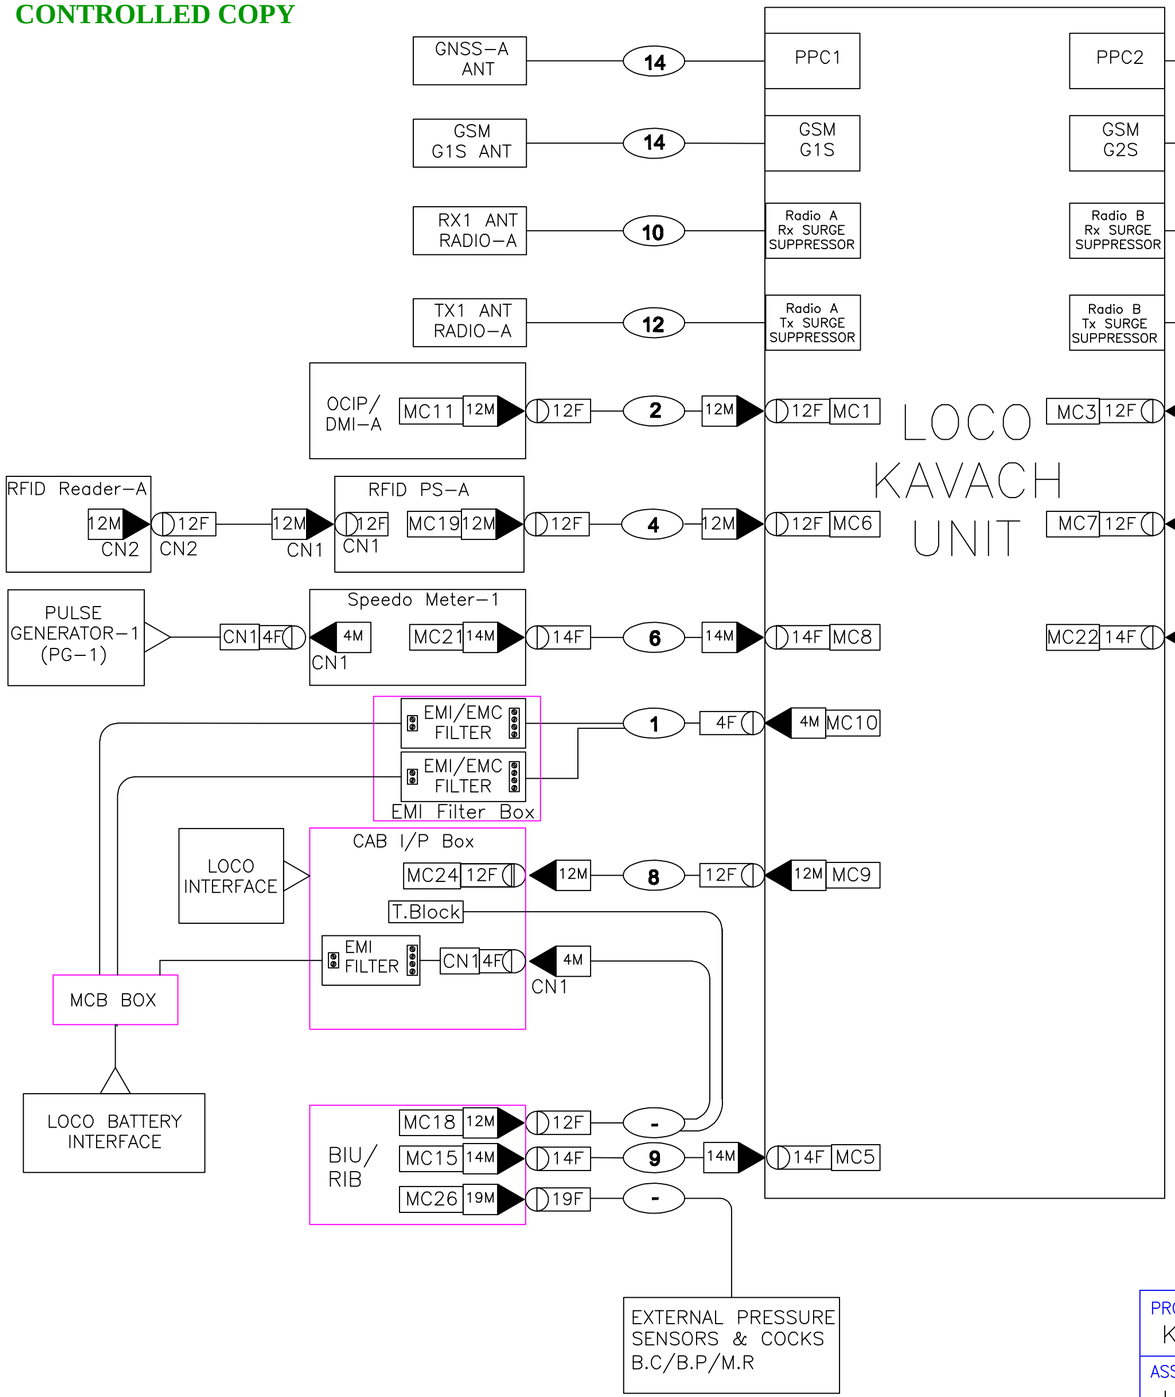


| # | SAPCODE | DESCRIPTION | QTY. | UNITS | Sheet No. |
|---|---|---|---|---|---|
| – | 6000051890 | HARNS–ASY_LOCO_KAVACH_4.0_EXTE_516490458 | 1.00 | PC | 1 |
| 1 | – | CABLE ASY_LOCO TCAS PWR SPLY | 1.00 | PC | 2 |
| 2 | – | CABLE ASY_OCIP/DMI–A SIG | 1.00 | PC | 3 |
| 3 | – | CABLE ASY_OCIP/DMI–B SIG | 1.00 | PC | 4 |
| 4 | – | CABLE ASY_RFID READER–A | 1.00 | PC | 5 |
| 5 | – | CABLE ASY_RFID READER–B | 1.00 | PC | 6 |
| 6 | – | CABLE ASY_SPEEDO METER–1 | 1.00 | PC | 7 |
| 7 | – | CABLE ASY_SPEEDO METER–2 | 1.00 | PC | 8 |
| 8 | – | CABLE ASY_CAB TERMINATION | 1.00 | PC | 9 |
| 9 | – | CABLE ASY_BIU SIGNAL | 1.00 | PC | 10 |
| 10 | – | CABLE ASY_LOCO LMR400 RD–A RX1 | 1.00 | PC | 11 |
| 11 | – | CABLE ASY_LOCO LMR400 RD–B RX2 | 1.00 | PC | 12 |
| 12 | – | CABLE ASY_LOCO LMR400 RD–A TX1 | 1.00 | PC | 13 |
| 13 | – | CABLE ASY_LOCO LMR400 RD–B TX2 | 1.00 | PC | 14 |
| 14 | – | CABLE ASSY_LMR 200_GPS_GSM ANT | 2.00 | PC | 15 to 16 |
| – | – | BOM SUMMARY SHEET | – | – | 17 |

Note:–

1. Connect the cable as per wiring diagram, route & secure with cable ties. Refer the each cable drawing for more connection details

| Sl.No. | Drawing No. | Item Description | Material Spec. | Qty. | Remarks |
|---|---|---|---|---|---|
| | | | | | |

PROJECT: KAVACH

ASSEMBLY: LOCO TCAS

SCALE: NTS | SIZE: A3 | SHEET: 1 OF 19

EFFECTIVE FROM:

ALL DIMENSIONS ARE IN mm

**HBL**

**HBL Power Systems Ltd.**

**(HBL RAIL)**

TITLE: **HARNS_ASY_LOCO_KAVACH_4.0_EXTE**

LOCO TCAS EXTERNAL WIRING BLOCK DIAGRAM

| | NAME | SIGN. | DATE |
|---|---|---|---|
| DRAWN | DLR | | |
| CHECKED | JP | | |
| APPROVED | YS | | |

DRAWING NO. 516490458 | REV. 1.1

PART NO. 6000051890

TOLERANCE NOT SPECIFIED SHALL BE AS PER IS : 2102 – 1993.

THIS DRAWING IS THE PROPERTY OF HBL POWER SYSTEMS LIMITED AND MUST NOT BE COPIED, REPRODUCED, TRANSMITTED OR DISCLOSED TO ANY THIRD PARTY WITHOUT THE WRITTEN CONSENT OF THE COMPANY.